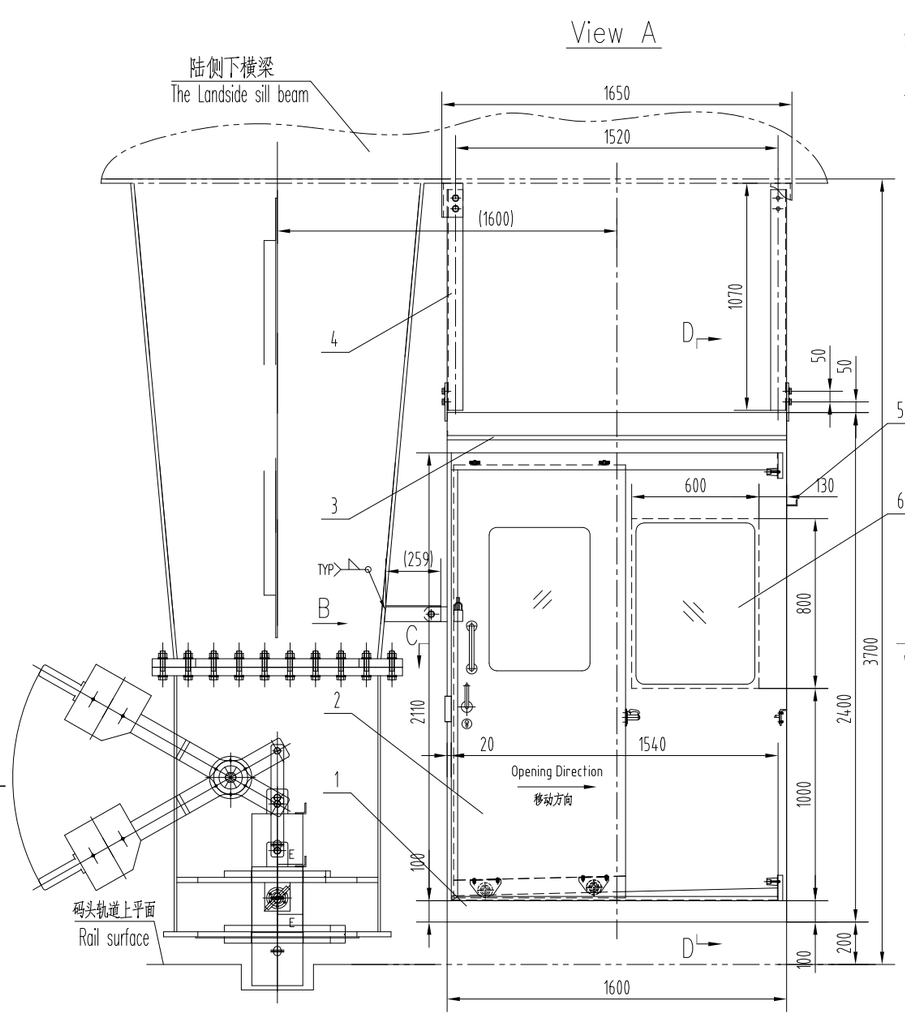
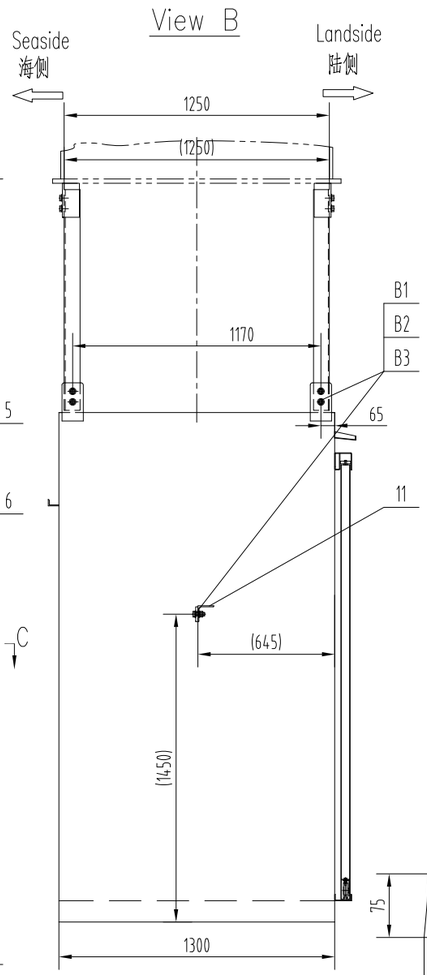
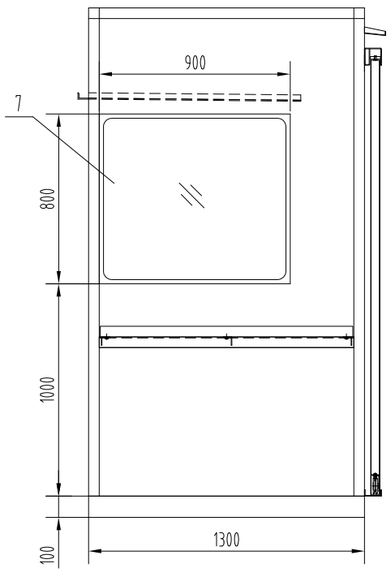
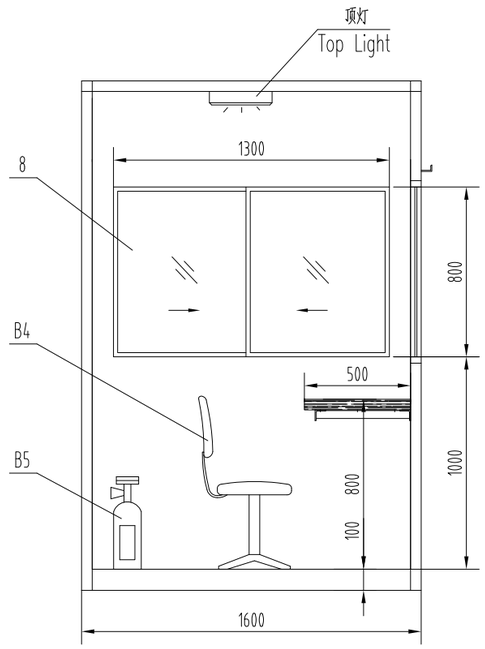
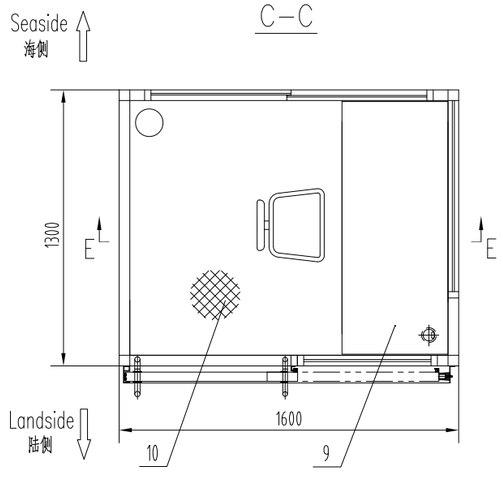
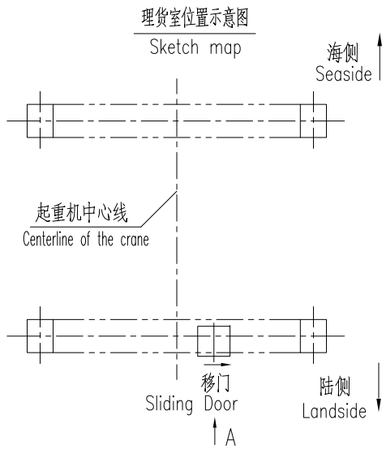












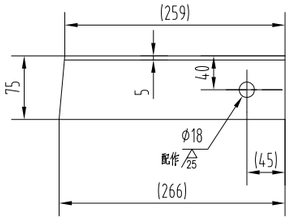


表1
Table 1

部位 Position	材料 Material
外包板 Outer plate	3mm 冷轧板 Steel plate –3
内包板 Inner plate	1.5mm 镀锌板 Galvanized plate –1.5
移窗 Sliding window	(3+0.38+3) 无色 夹层安全玻璃 None-tinted laminated safety glass
固定窗 Fixed window	(5+0.38+5) 无色 夹层安全玻璃 None-tinted laminated safety glass

技术要求

1. 外部焊缝均为连续焊,所有焊缝均需符合AWS D1.1-2006.
2. 防松螺母M16(B2)的预紧力矩为200Nm

Technical requirements

1. All exterior welds shall be continuous.
   All welds shall accord to AWS D1.1-2006.
2. The pretightening torque of M16(B2) is 200Nm.

NO.	SUB-NO. OR STDD	VER	NAME & SIZE	MTRL	QTY	EACH	TOTAL	NOTE
B5			二氧化碳灭火器 MTZ2 Fire extinguisher	外购成品 Pur.	1	9.0	9.0	'带支架' With support
B4			转椅 Revolving chair	外购成品 Pur.	1	6.0	6.0	
B3	GB/T95-85		平垫圈 16 Washer	100HV	18	0.0	0.0	'Dacro'
B2	ZN6175-T-SL		六角凸缘自锁防松螺母 M16 Nut	08H	9	0.0	0.0	'Dacro'
B1	GB5783-86		螺栓 M16×45 Bolt	8.8	9	0.1	0.8	'Dacro'
11	GB9787-88		角钢 75×75×5 l=(266) L-bar	Q235-A	1	1.5	1.5	
10			耐压防滑橡胶地毯 -4 A=1.8 rubber matting	橡胶 Rubber	1	9.0	9.0	'黑色' Black
9	ZT2-032211-00	0	工作台1 Work table 1	部件 Ass.	1	50.0	50.0	
8	ZT2-032231-00	0	移窗1 Sliding window 1	组件 Ass.	1	20.0	20.0	
7	ZT2-032222-00	0	固定窗2 Fixed window 2	组件 Ass.	1	19.8	19.8	
6	ZT2-032221-00	0	固定窗1 Fixed window 1	组件 Ass.	1	13.4	13.4	
5	ZT2-032241	0	窗雨檐1 Rain Shield of window 1	Q235-A	1	4.3	4.3	
4	J526A3303	0	支架1 Support 1	焊接件 Wel.	1	32.0	32.0	
3	ZT2-030733	0	雨檐3 Rain Shield 3	焊接件 Wel.	1	4.6	4.6	
2	J526A3302	0	移门B-2015 Sliding Door B-2015	组件 Ass.	1	125.5	125.5	右移 Right style
1	J526A3301	0	理货室结构1 Cab Structure 1	焊接件 Wel.	1	743.1	743.1	

工号/JOB NO. ZP12-1873			项目名称/PROJECT SliLanka CICT 12 STS Cranes				
设计/DSGN	校对/CHKD	审核/EXAM	审定/APPD	图幅/FORMAT			
日期/DATE	日期/DATE	日期/DATE	日期/DATE	A2			
材料/MAT 部件总图 Ass.		比例/SCALE 1:20	图名/DRAWING NAME 理货室 Check's Cab				
单重/WEI (Kg) 1039							
修改标志/Sign	ZPMC 上海振华重工集团		图号/DRAWING NO. J526A3300	版本/REV 0	页号/PAGE 1		

010102