




REV	DATE	BY	DESCRIPTION
01	2012/07/05	Zhangjun	
02	2012/08/17	Zhangjun	

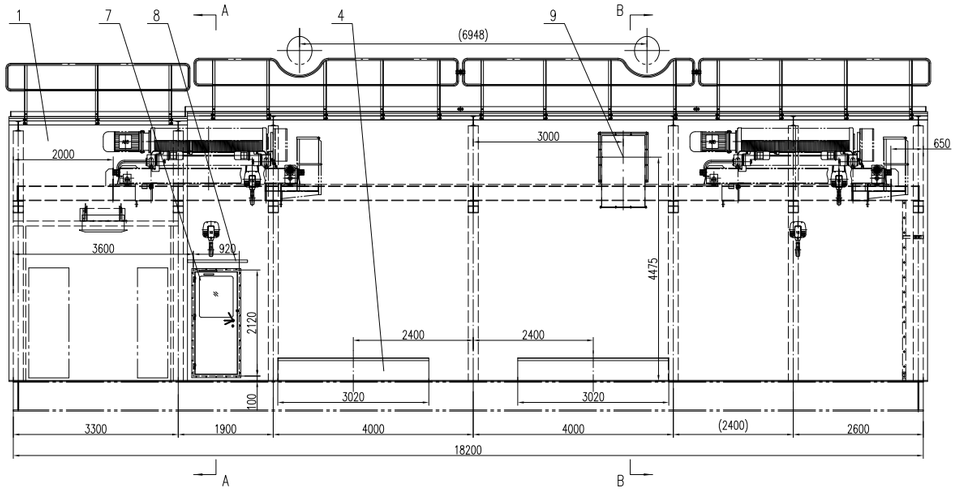

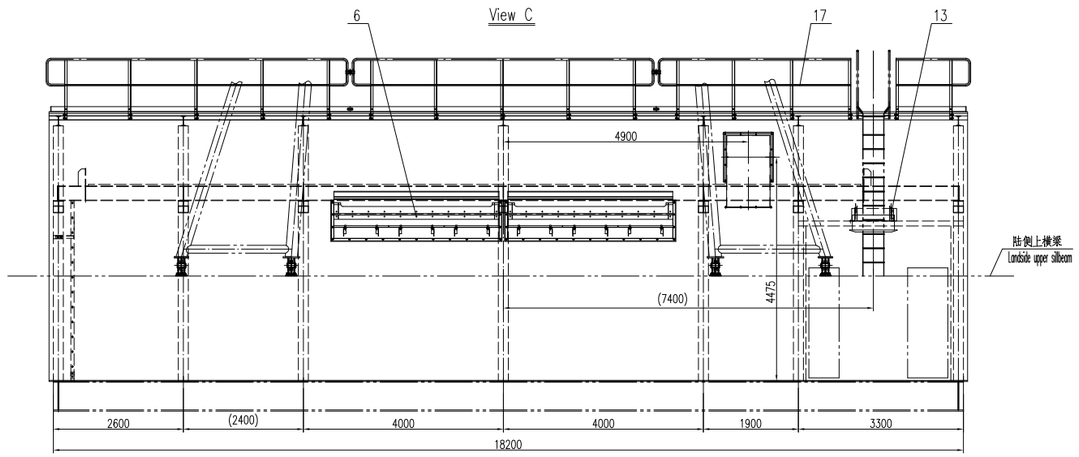

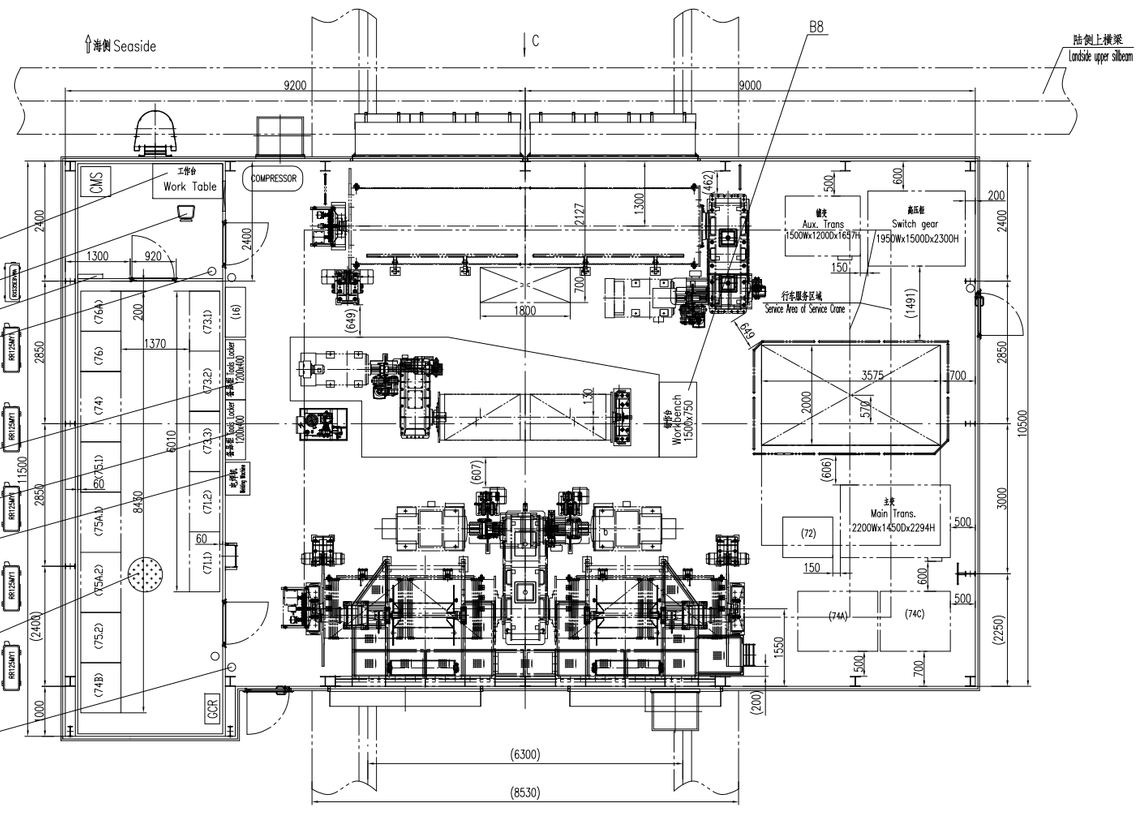

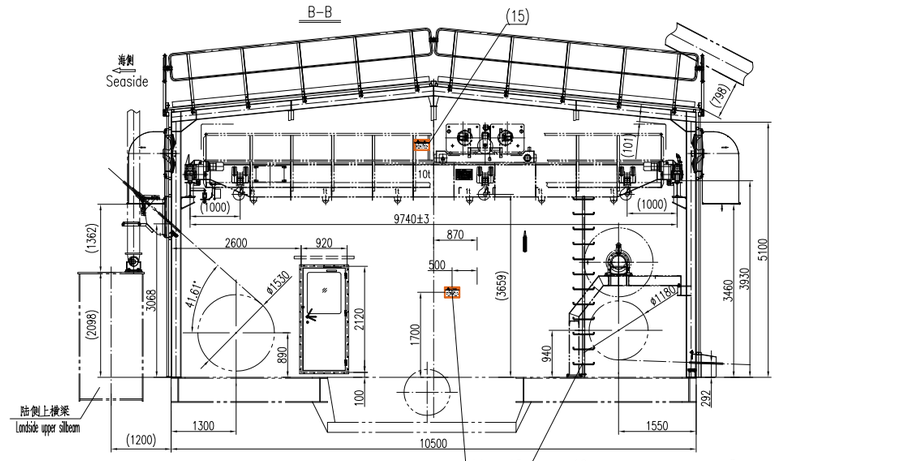

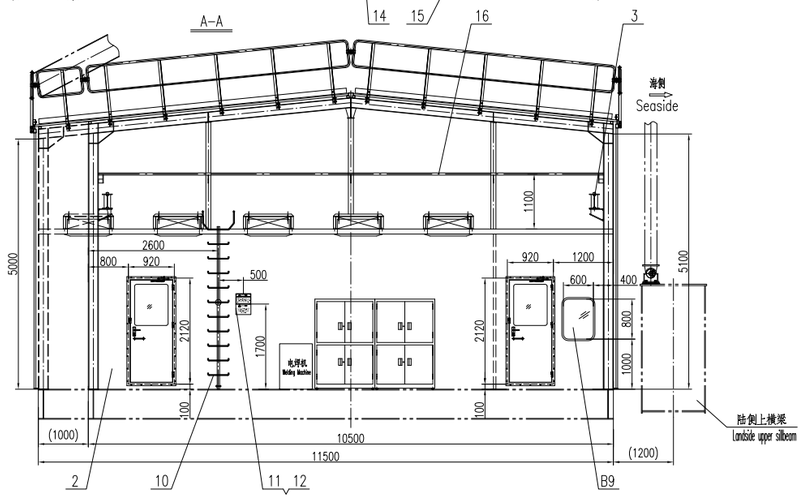

技术要求

1. 机器房结构现场焊接于机房底盘上,焊接按机房结构图要求.焊缝均按AWS D1.1—2006标准制造与验收.
2. 行车承轨梁的牛腿在焊接到立柱上之前,应先确认行车小车在陆侧极限位置时,不要与屋顶横梁干涉.

Technical requirements

1. Machinery House is welded on house base in site, Welding according to its structure requirement. Welding are checked according to AWS D1.1—2006.
2. Before supports are welded to post,trolley is not interfered with roof of house when it is located in the limited position of landside.

PROJECT: Sri Lanka CICT 12 STS Cranes					DESIGN STAGE:		SCALE:	1:60
ITEM NAME: 机器房 Machinery House					DRAW NO: J526A3000			
ZPMC	DSGN				TRACE		APP.	组件 Ass.
	DRAW				CHCK		Q'TY/SET	1
	CHCK				VER.		SET/CRANE	33693kg

明 细 表
SUBSIDIARY LIST

*The quantity and weight of this list is to one set
*此表为一套的数量和重量
_1_set/crane, 33368 kg/set, kg/crane

设计：
校对：

PROJECT NAME or CODE: 斯里兰卡CICT码头12台65T岸桥			SUB-PART NAME: 机器房 Machinery House		SUB DRAW NO: J526A30		
序号 NO.	图号或标准 SUB-NO.or STDD	名称与规格 NAME & SIZE	材料或型号 MTRL or STYLE	每套数量 Q'TY/SET	单重 PIECE WGHT	总重 TOTAL WGHT	备注 NOTE
1	J526A3001	机器房围棚结构 Machinery House Structure	焊接件 Welded	1		23587	
2	J526A3002	电气房围棚结构 Electrical Room Structure	组件 Assembly	1		2425	
3	J526A3003	维修行车轨道 Maintenance Lift Rail	焊接件 Welded	2	1396	2792	对称制作 Made Symmetrically
4	J526A3004	起升出绳罩 Main Hoist Rope's Hood	组件 Assembly	2	163	326	
5		-4耐压橡胶地毯 Rubber Mat		22m^2		141	
6	J526A3005	俯仰出绳罩 Boom Rope's Hood	组件 Assembly	2	541	1082	
7	J526A3006	机房门的布置 Layout of M.House door	组件 Assembly	1		722	
8	ZT2-030741	雨镟A1 Drip Shield A1	焊接件 Welded	2	7	14	通用标准件
9	ZT2-030401-00a	排风扇 Ventilation Fan (Exaust)	组件 Assembly	2	135.5	271	三表另发 Tabulation by others
10	J526A3007	直梯1 Ladder1	焊接件 Welded	1		61	
11	ZT2-032722	警示牌2 Warning Sign 2	自粘性乙烯 ethylene paster	1		1	通用标准件
12	ZT2-032721	警示牌1 Warning Sign 1	自粘性乙烯 ethylene paster	1		1	通用标准件
13	J526A3008	空调安装支架 A.C Support	焊接件 Welded	1		98	
14	ZT2-032726	警示牌6 Warning Sign 6	聚丙烯板材 polypropylene plate.	2	1	2	通用标准件
15	J526A3009	直梯2 Ladder2	焊接件 Welded	1		57	
16	J526A3010	保险杠 Security pole	组件 Assembly	1		37	
17	J525A3011	屋顶栏杆 Handrail of Roof	组件 Assembly	1		763	
		焊缝 Weld Material				324	按总重的1%计算 1% total weight

ZPMC

明 细 表
SUBSIDIARY LIST

*The quantity and weight of this list is to one set
*此表为一套的数量和重量
_1_set/crane, 33368 kg/set, kg/crane

设计：
校对：

PROJECT NAME or CODE: 斯里兰卡CICT码头12台65T岸桥			SUB-PART NAME: 机器房 Machinery House			SUB DRAW NO: J526A30	
序号 NO.	图号或标准 SUB-NO.or STDD	名称与规格 NAME & SIZE	材料或型号 MTRL or STYLE	每套数量 Q'TY/SET	单重 PIECE WGHT	总重 TOTAL WGHT	备注 NOTE
B1		工作台(1200x700) Desk	组件 Assembly	1		75	
B2		转椅 Chair	组件 Assembly	1		14	
B3		CO2灭火器 Fire Extinguisher	MTZ2	2	9	18	自带支架 With support
B4	ZT2-032603	备品柜 Tools Locker	LK120/40	1		100	通用标准件
B5	ZT2-032603	备品柜 Tools Locker	LK120/40-B	1		100	通用标准件
B6	380V,50HZ,3~	电焊机 Welding Machine	ZEXI-500	1		173	配25m龙头线和接地线 With 25m cable
B7		CO2灭火器 Fire Extinguisher	MTZ5	3	21	63	自带支架 With support
B8	ZT2-032604	钳作台 Work Bench	WB150/75	1		100	通用标准件
B9	ZT2-032601	电气室固定窗 Fixed Window	FWE 8/6	1		21	通用标准件
B10		铝合金人字梯 L=1.5m ladder	铝合金 aluminium alloy	1		10	