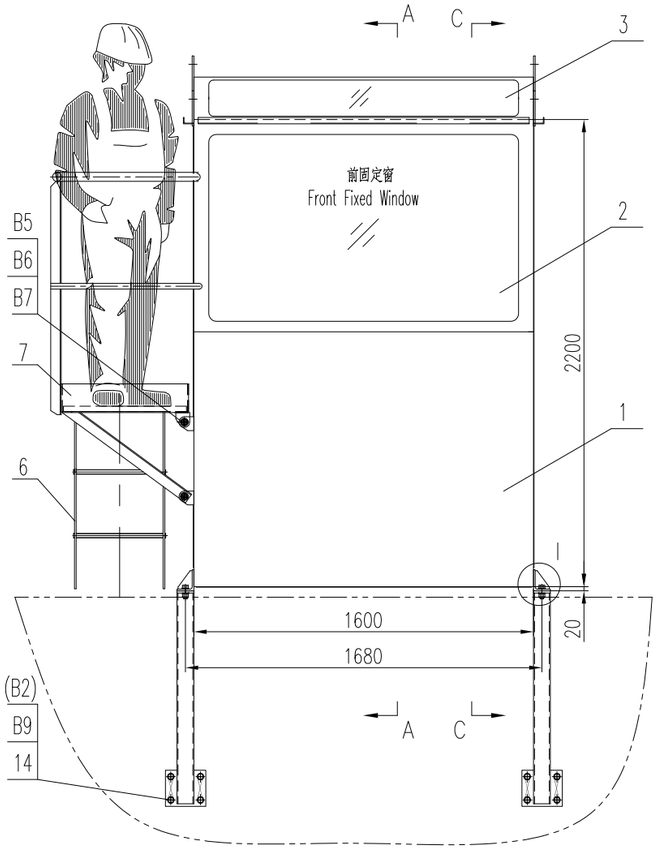
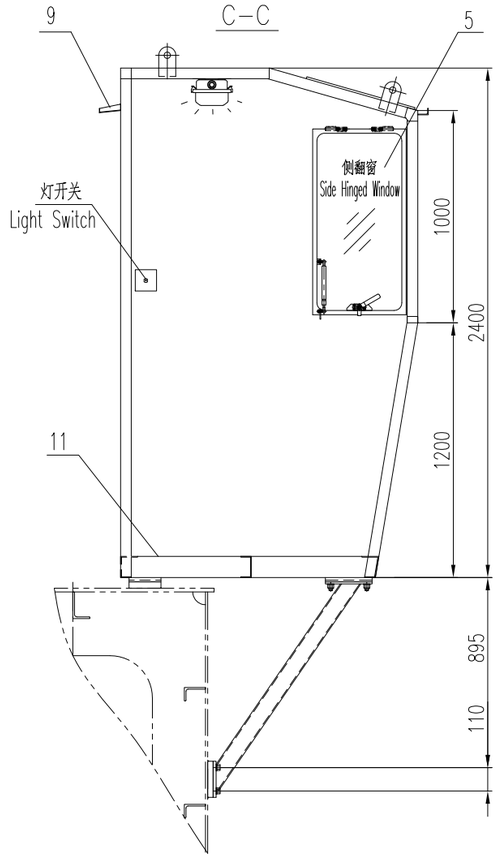
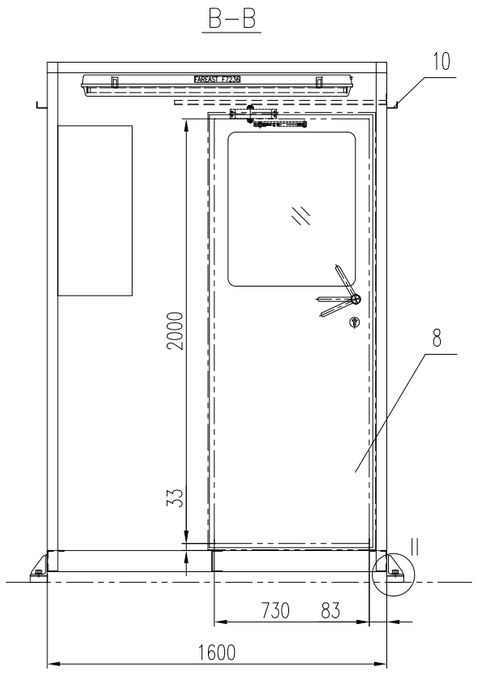
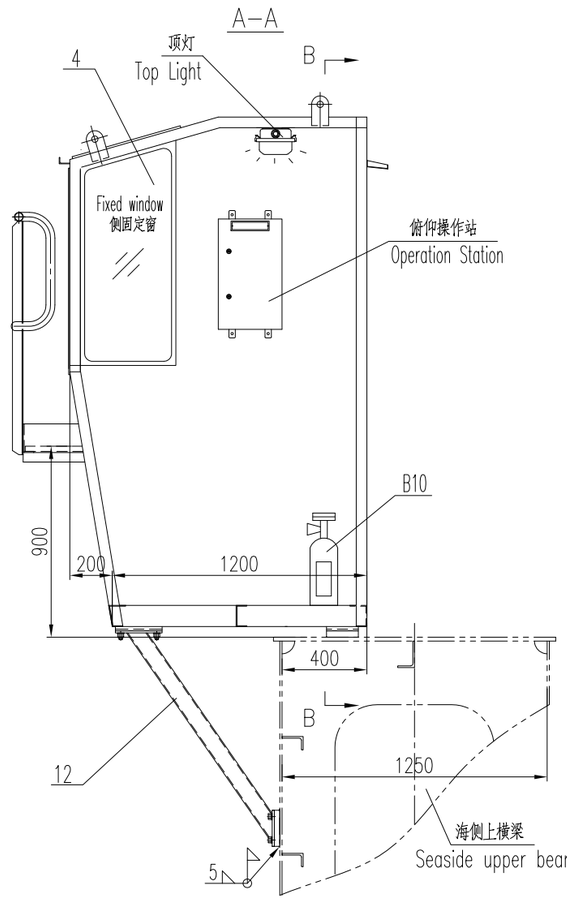
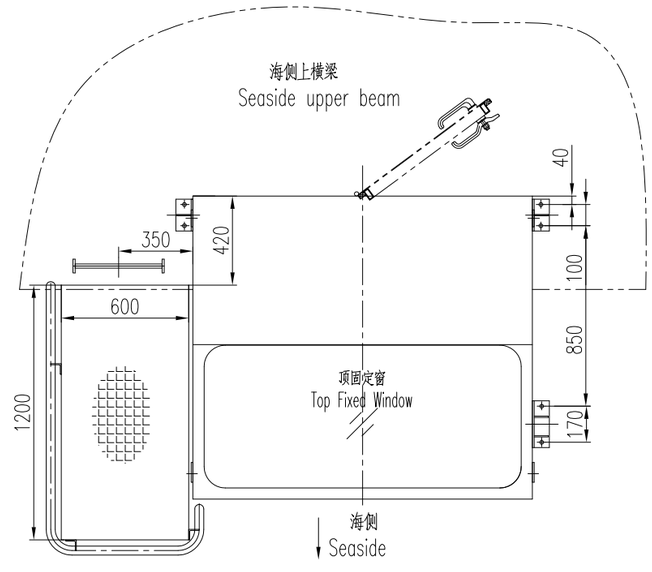
REV	DATE	BY	DESCRIPTION
1	2012.05.30	LiuBin	











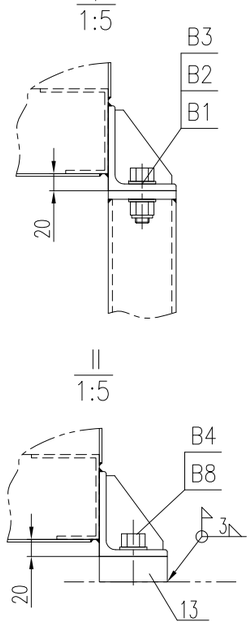


表1
Table 1

部位 Position	材料 Material
外包板 Outer plate	3mm 冷轧板 Steel plate –3
内包板 Inner plate	1.5mm 镀锌板 Galvanized plate –1.5
侧固定窗&侧翻窗 Side window	(3+0.38+3) 无色 夹层安全玻璃 None-tinted laminated safety glass
前固定窗 Front fixed window	(5+0.38+5) 无色 夹层安全玻璃 None-tinted laminated safety glass
顶固定窗 Top fixed window	(5+0.38+5) 无色 夹层安全玻璃 None-tinted laminated safety glass

技术要求
1. 外部焊缝均为连续焊,所有焊缝均需符合AWS D1.1-2006.
2. 防松螺母预紧力矩:M16(B3)--200Nm,M20(B7)--410Nm.

Technical requirements
1. All exterior welds shall be continuous.
   All weldS shall accord to AWS D1.1-2006.
2. The pretightening torque of nut(ZN6175-T-SL)
   M16(B2)--200Nm, M20(B7)--410Nm.

工号/JOB NO. ZP12-1873			项目名称/PROJECT SliLanka CICT 12 STS Cranes	
设计/DSGN	校对/CHKD	审核/EXAM	审定/APPD	图幅/FORMAT A2
日期/DATE	日期/DATE	日期/DATE	日期/DATE	
材料/MAT 部件总图Ass.		比例/SCALE 1:20	图名/DRAWING NAME 大梁俯仰操作室 Boom hoist operator's cab	
单重/WEI(Kg) 1050				
修改标志/Sign	ZPMC 上海振华重工集团		图号/DRAWING NO. J526A3200	版本/REV 0 / 页号/PAGE 1

010102

明 细 表
SUBSIDIARY LIST

*The quantity and weight of this list is for one set

*此表为一套的数量和重量

设计：

_1035_ kg/set, __1__ set/crane, __1035__ kg/crane

校对：

PROJECT NAME or CODE: 斯里兰卡CICT码头桥吊			SUB-PART NAME: 大梁俯仰操作室			SUB DRAW NO: J526A3200	
序号 NO.	**图号或标准 SUB-NO.or STDD**	**名称 NAME**	**规格或型号 SIZE & STYLE**	**材料 MTRL**	**每套数量 Q'TY/SET**	**单重 PIECE WGHT**	**总重 TOTAL WGHT**
1	ZT2-031912-00a	Cab Structure 2A 操作室结构2A		Welded 焊接件	1	683.3	683.3
2	ZT2-032001-00	Front fixed window 1 前固定窗1		Safety glass 安全玻璃	1	36.8	36.8
3	ZT2-032021-00	Top fixed window 1 顶固定窗1		Safety glass 安全玻璃	1	24.6	24.6
4	ZT2-032011-00	Side fixed window 1 侧固定窗1		Safety glass 安全玻璃	1	7.6	7.6
5	ZT2-032016-00	Side hinged window 1 侧翻窗1		Safety glass 安全玻璃	1	16.4	16.4
6	ZT2-032041-00	Ladder 小直梯		Ass. 组件	1	13.8	13.8
7	ZT2-032031	Platform 小平台		Ass. 组件	1	77.6	77.6
8	ZT2-030246-00	Hinged door C1-2073 铰链门C1-2073	铰链型号:I型 右外开	Ass. 组件	1	86.4	86.4
9	ZT2-030731	Rain Shield 1 雨锯1		Welded 焊接件	1	2.8	2.8
10	ZT2-032061	Rain Shield 窗雨锯		Welded 焊接件	1	4.7	4.7
11		Black Rubber Carpet 黑色绝缘橡胶地毯 t=4	1.7m^2	Rubber 橡胶	1	8.5	8.5
12	ZT2-032051	Support 支架		Welded 焊接件	2	27	54
13	ZT2-032056	Seat 支座		Welded 焊接件	2	2.8	5.6
14		不锈钢钢丝Φ2 Stainless steel	1.3m	不锈钢 Stainless steel	1		0
							0
B1	GB5783-86	螺栓 Bolt M16x45	8.8级 Grade	达克罗Dacro	4	0.1	0.4
B2	GB95-85	垫圈 Washer 16	100HV	达克罗Dacro	12	0.0951	1.1412
B3	ZN6175-T-SL	防松螺母 Nut M16	8级 Grade	达克罗Dacro	4	0.032	0.128
B4	GB5783-86	螺栓 Bolt M16x35	8.8级 Grade	达克罗Dacro	4	0.1	0.4
B5	GB5783-86	螺栓 Bolt M20x50	8.8级 Grade	达克罗Dacro	4	0.2	0.8
B6	GB95-85	垫圈 Washer 20	100HV	达克罗Dacro	8	0.0144	0.1152
B7	ZN6175-T-SL	防松螺母 Nut M20	8级 Grade	达克罗Dacro	4	0.058	0.232
B8	GB854-88	垫圈 Washer 16		达克罗Dacro	4		0
B9	GB32.1-88	螺栓 Bolt M16x35	8.8级 Grade	达克罗Dacro	8	0.1	0.8
B10		二氧化碳灭火器(带支架)	MTZ2		1	9	9